


Item 07 Brookshire

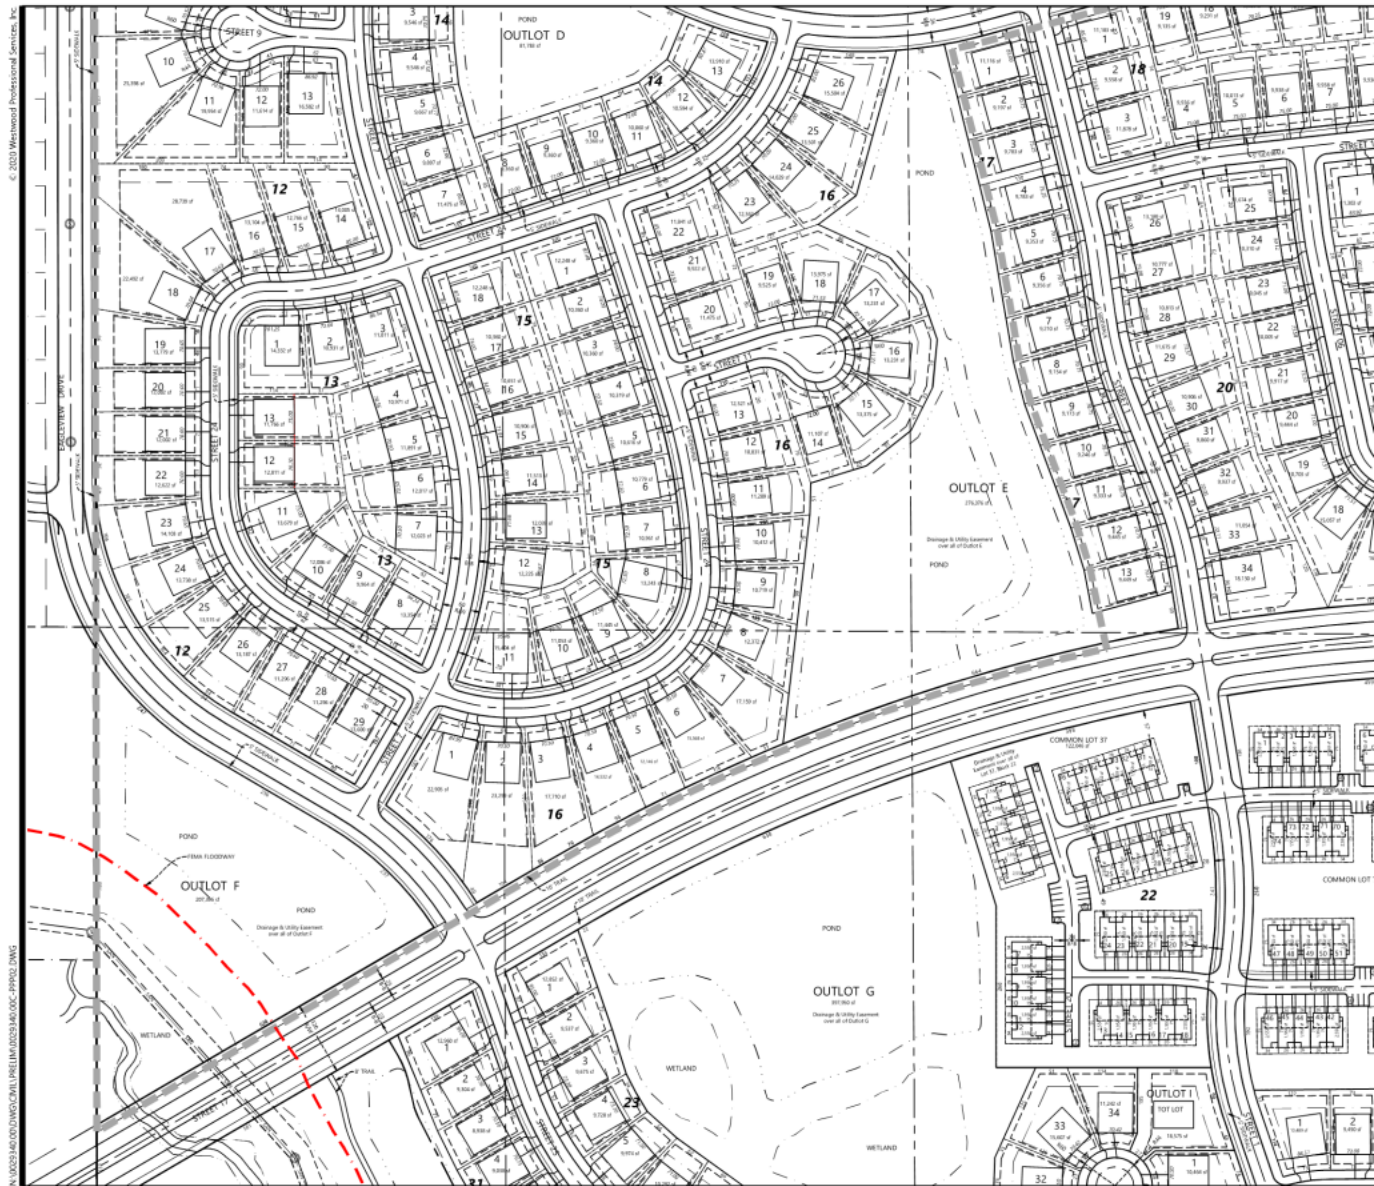

DESIGNED: CHECKED: DRAWN: HORIZONTAL SCALE: 1"=100' VERTICAL SCALE: 1"=20' OR 10'	INITIAL ISSUE: 02/17/22 REVISIONS: 03/24/2022 REVISED PER CITY COMMENTS	PREPARED FOR: DR HORTON, INC. - MINNESOTA 20860 KENBRIDGE COURT, SUITE 100 LAKEVILLE, MINNESOTA 55044	I HEREBY CERTIFY THAT THIS PLAN WAS PREPARED BY ME OR UNDER MY DIRECT SUPERVISION AND THAT I AM A FULLY LICENSED LANDSCAPE ARCHITECT UNDER THE LAWS OF THE STATE OF MINNESOTA. CORY MEYER DATE 03/24/2022 LICENSE NO. 26971	BROOKSHIRE LAKEVILLE, MINNESOTA	W Phone Fax Toll Free Website
---	---	---	---	---	--

